


Bei Bedarf:
Aufstellung von VZ 283 / 286
mit Gültigkeitsangabe
ab/am : Datum und Uhrzeit
min. 4 Tage im Voraus.

Der provisorischen Beschilderung
widersprechende Verkehrszeichen
und Wegweisung sind abzudecken

Erstellt	Name	Zeichen
11.03.2024	Heck	
Änderung	Name	Zeichen
22.04.2024	Heck	
16.05.2024	Heck	
04.07.2024	Heck	
Genehmigt	Name	Zeichen

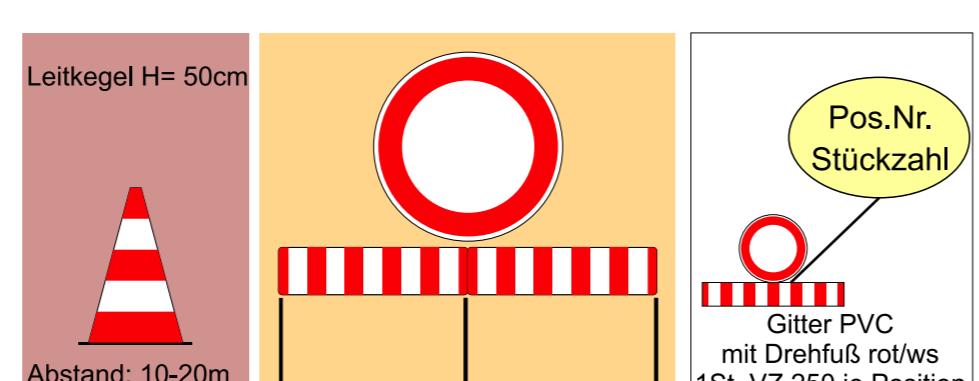


Schwimmen 1,6 km
Radfahren 35 km
Laufen 10 km

Bauphase: 01 Plan Nr.: Ü 01
Baumaßnahme: Heidelbergman 2024


Auftraggeber: Heidelbergman
von: 28.07.2024 bis: 28.07.2024

Heck GmbH
Verkehrstechnik
info@heck-verkehrstechnik.de
Tel: 06233-3531109 Fax: 06233-3533942

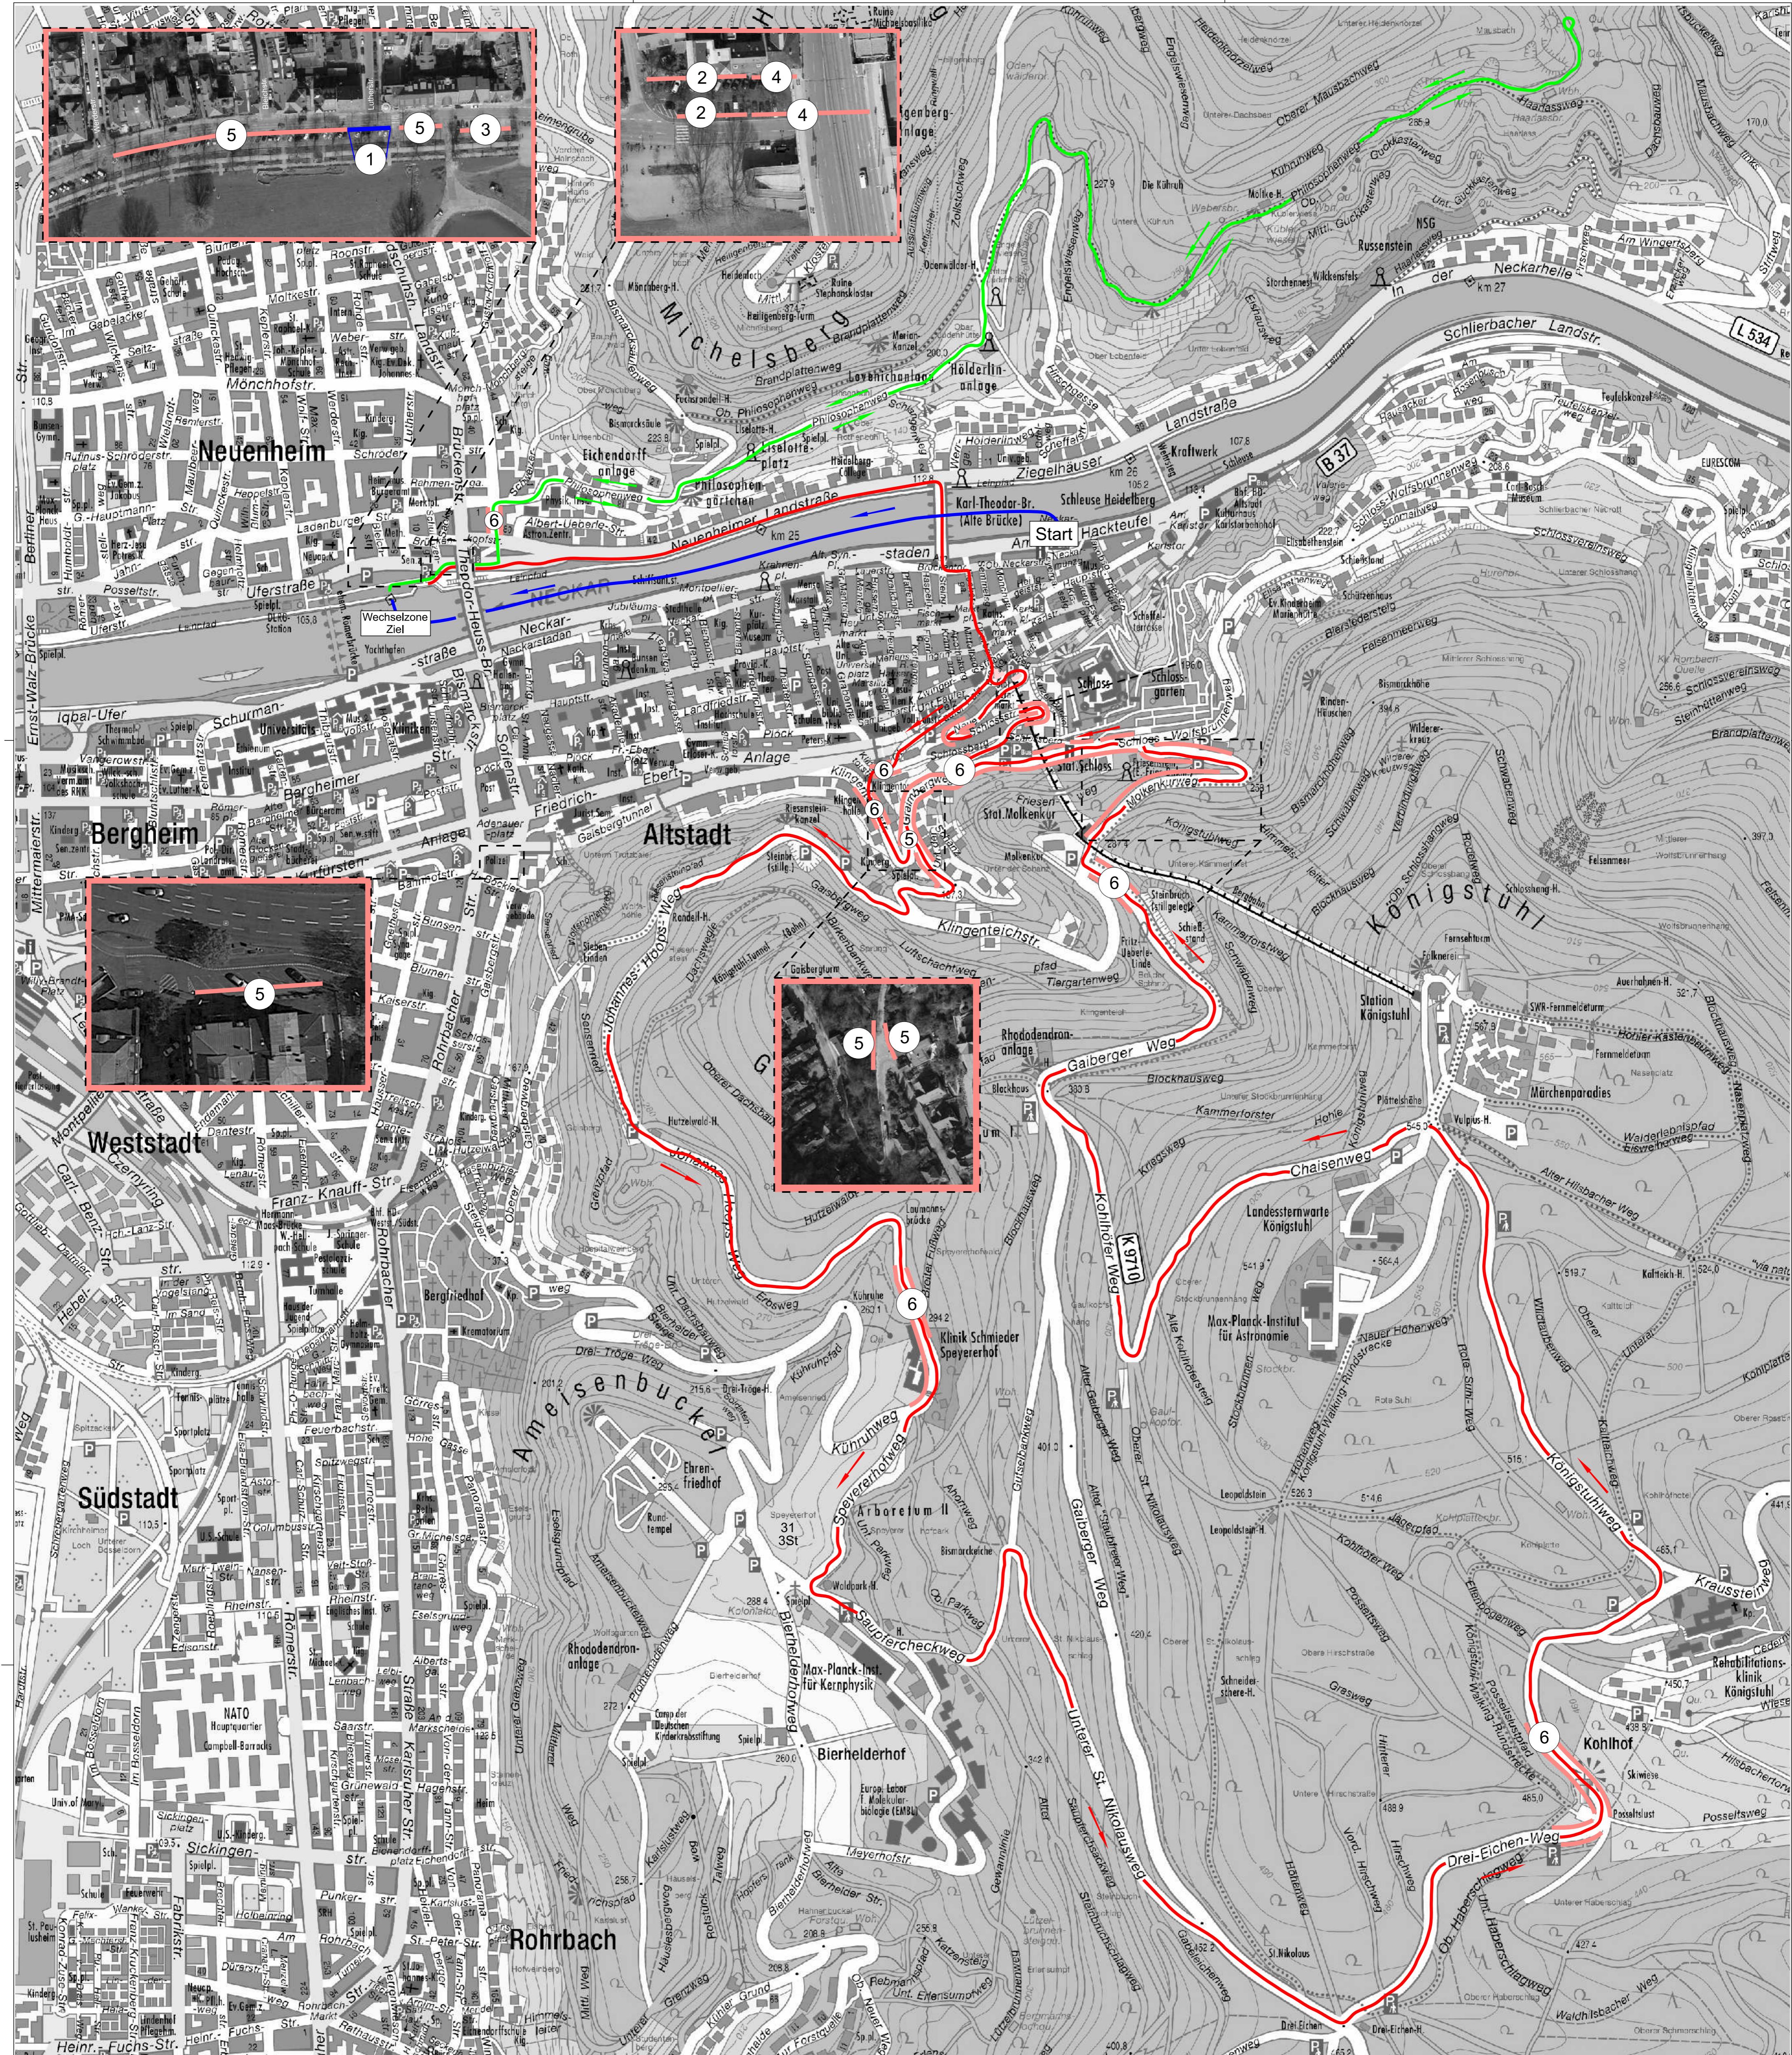

Bei Bedarf:
Aufstellung von VZ 283 / 286
mit Gültigkeitsangabe
ab/am : Datum und Uhrzeit
min. 4 Tage im Voraus.

Erstellt	Name	Zeichen
11.03.2024	Heck	
Änderung	Name	Zeichen
24.04.2024	Heck	
16.05.2024	Heck	
04.07.2024	Heck	
Genehmigt	Name	Zeichen

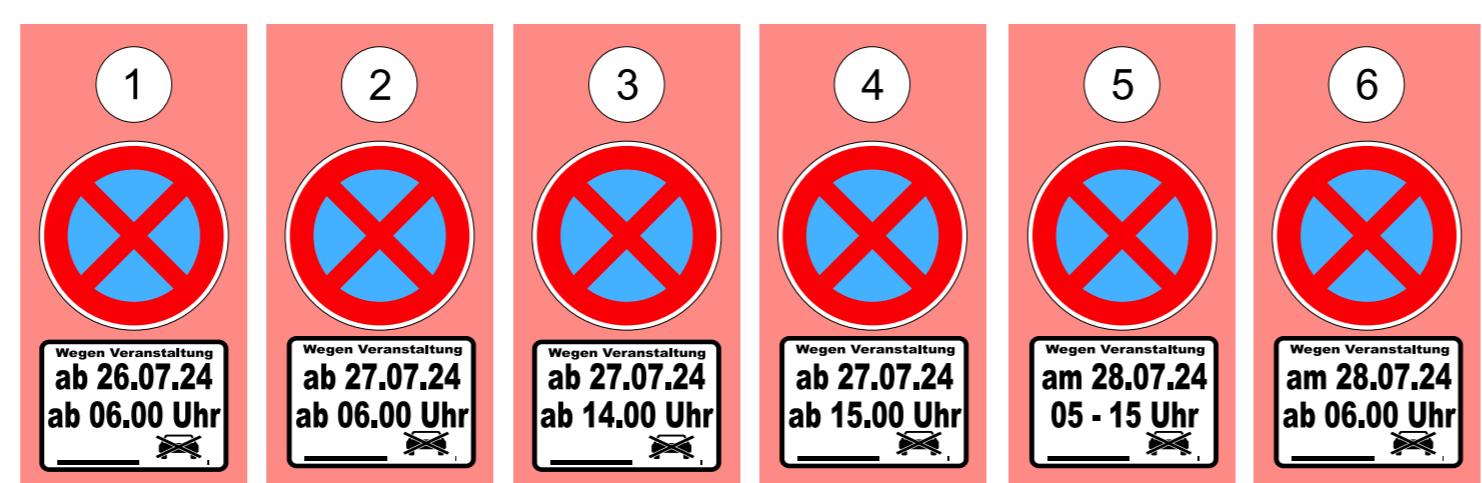

Schwimmen 1,6 km
Radfahren 35 km
Laufen 10 km

Der provisorischen Beschilderung
widersprechende Verkehrszeichen
und Wegweisung sind abzudecken

Bauphase:	Plan Nr.: VZ 283
Baumaßnahme:	Heidelbergman 2024
Auftraggeber:	Heidelbergman
von:	28.07.2024
bis:	28.07.2024
Heck	GmbH
Verkehrstechnik	
info@heck-verkehrstechnik.de	
Tel: 06233-3531109 Fax: 06233-3533942	